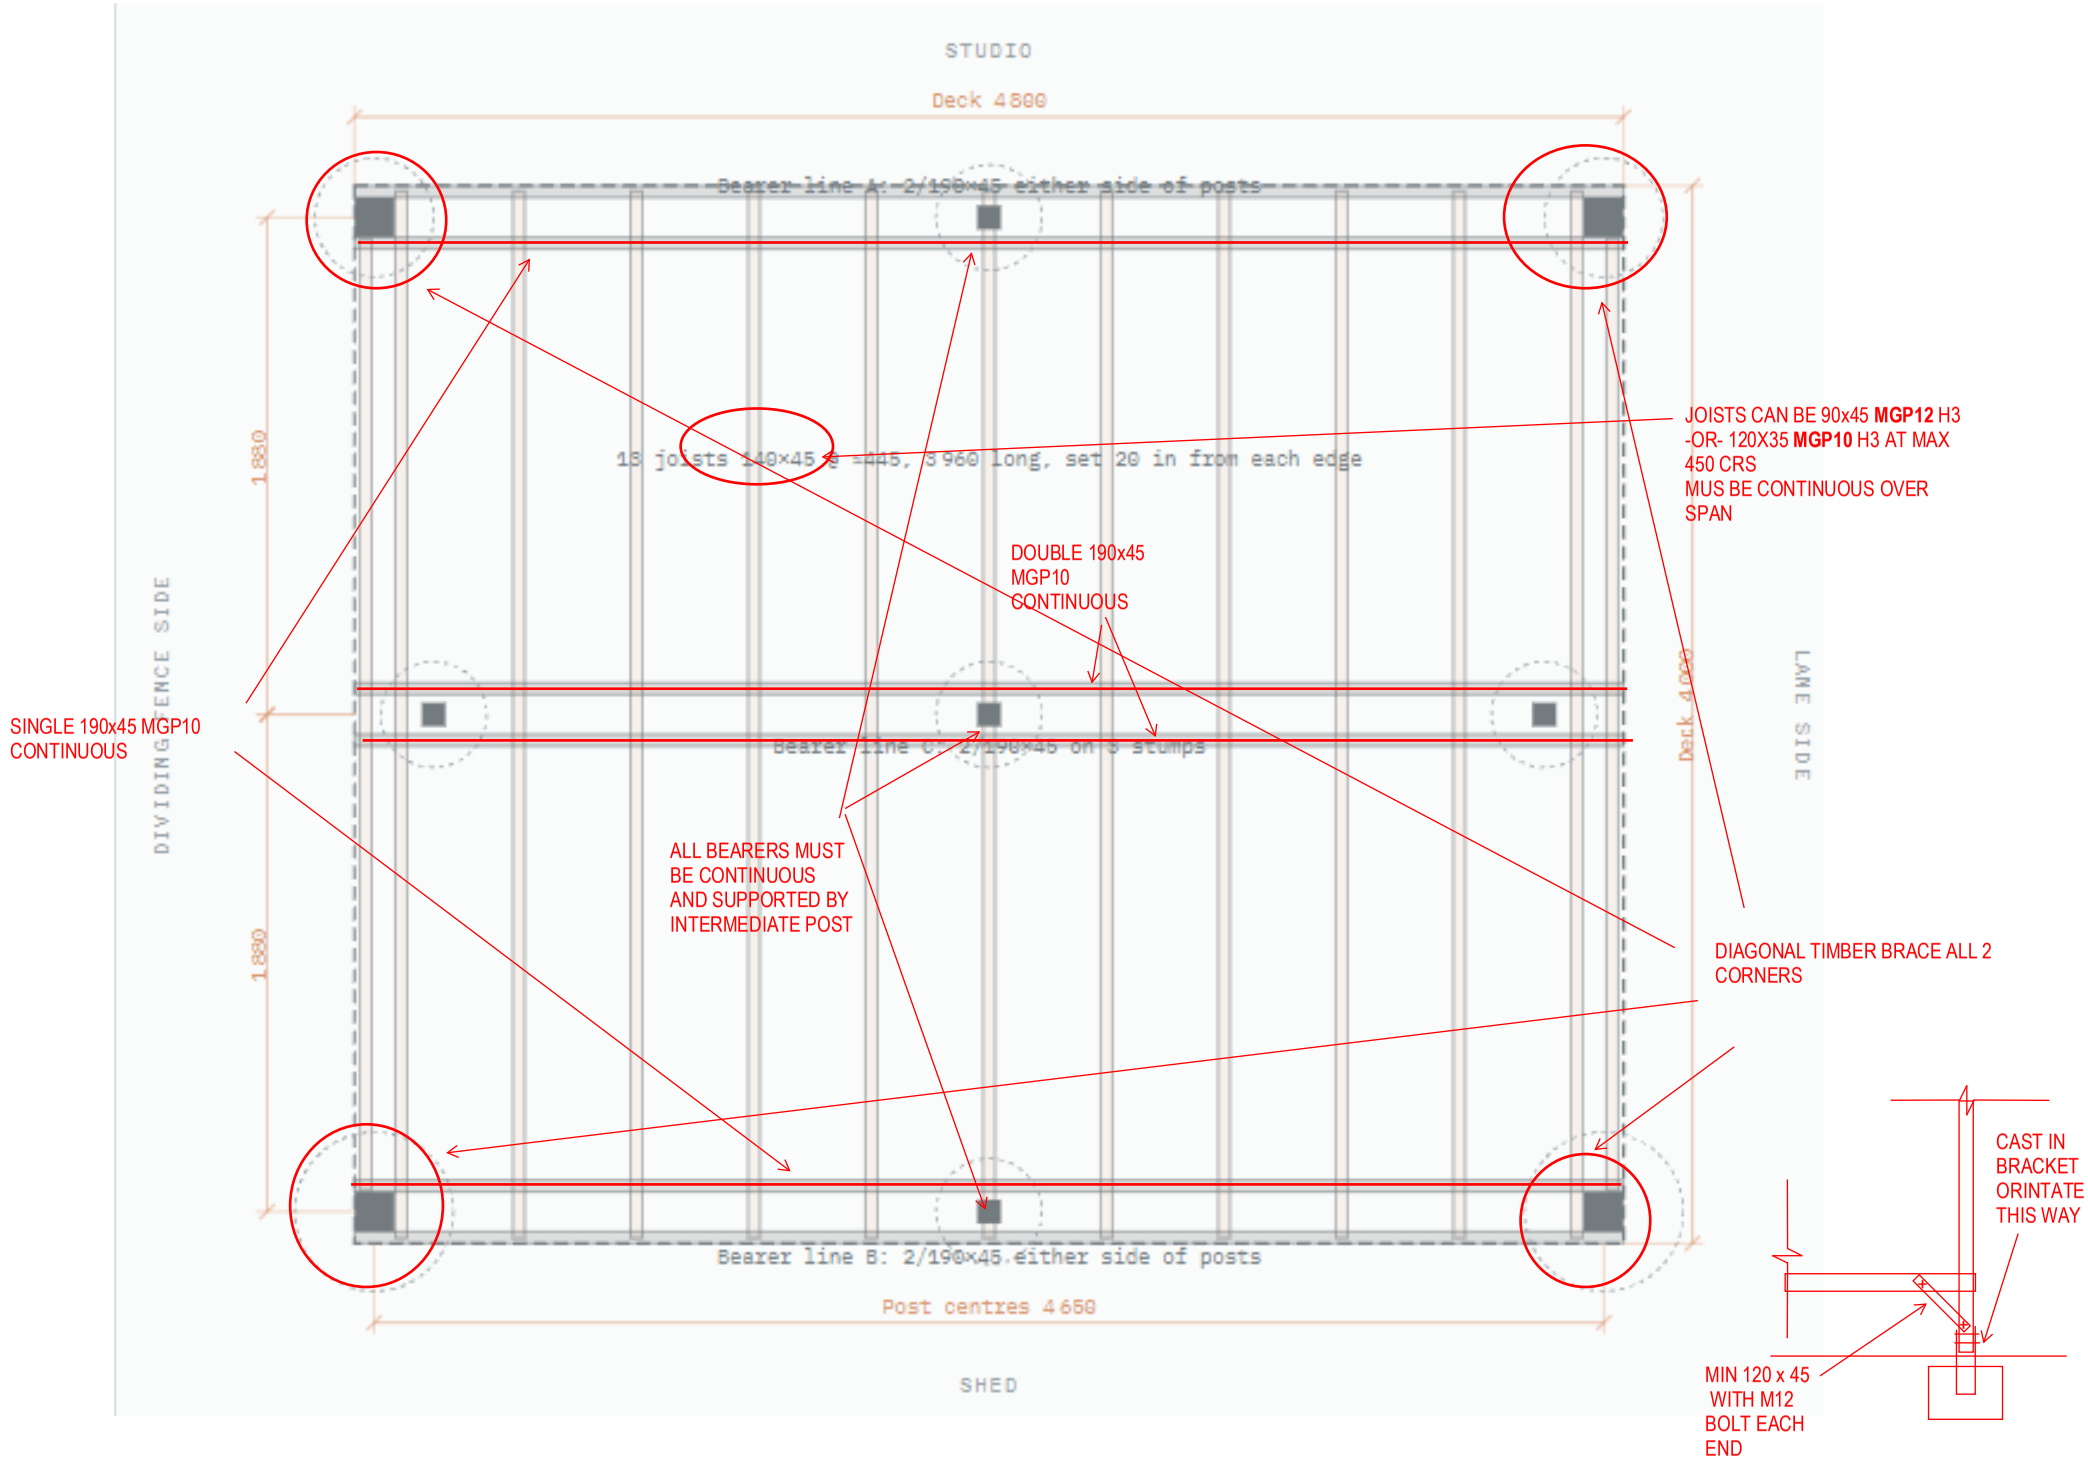
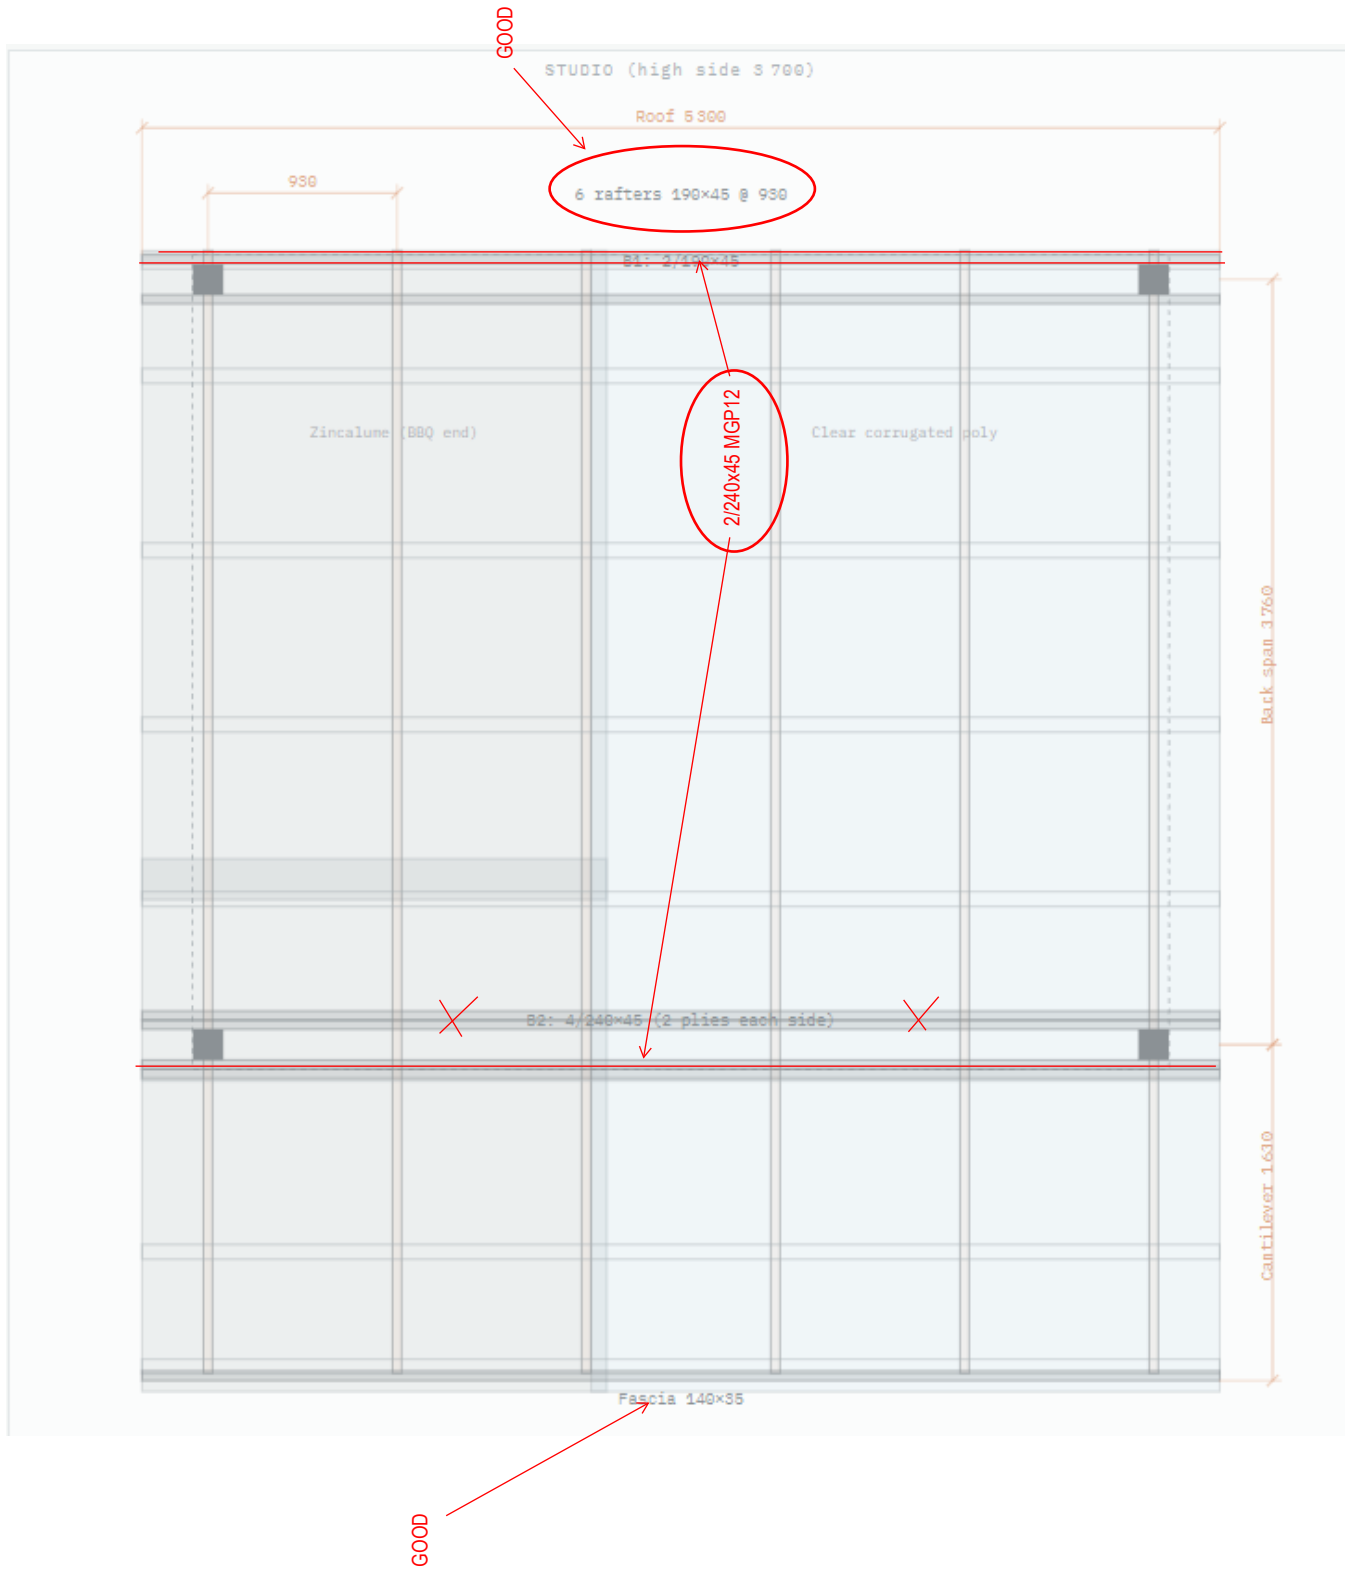

STUDIO
Deck 4800
Bearer line A: 2/190x45 either side of posts
18 joists 140x45 @ =445, 3960 long, set 20 in from each edge
DOUBLE 190x45
MGP10
CONTINUOUS
JOISTS CAN BE 90x45 MGP12 H3
-OR- 120X35 MGP10 H3 AT MAX
450 CRS
MUS BE CONTINUOUS OVER
SPAN
SINGLE 190x45 MGP10
CONTINUOUS
Bearer line C: 2/190x45 on 3 stumps
ALL BEARERS MUST
BE CONTINUOUS
AND SUPPORTED BY
INTERMEDIATE POST
DIAGONAL TIMBER BRACE ALL 2
CORNERS
1880
1880
DIVIDING FENCE SIDE
LANE SIDE
Deck 4000
Bearer line B: 2/190x45 either side of posts
Post centres 4650
SHED
CAST IN
BRACKET
ORINTATE
THIS WAY
MIN 120 x 45
WITH M12
BOLT EACH
END


GOOD
STUDIO (high side 3 700)
Roof 5 300
930
6 rafters 190×45 @ 930
B1: 2/190×45
Zincalume (BBQ end)
2/240x45 MGP12
Clear corrugated poly
Bark span 3760
B2: 4/240×45 (2 plies each side)
Cantilever 1 630
Fascia 140×35
GOOD